
Drawing and design are the property of Vastu Shilpa Consultants and are not to be copied or used without their permission.

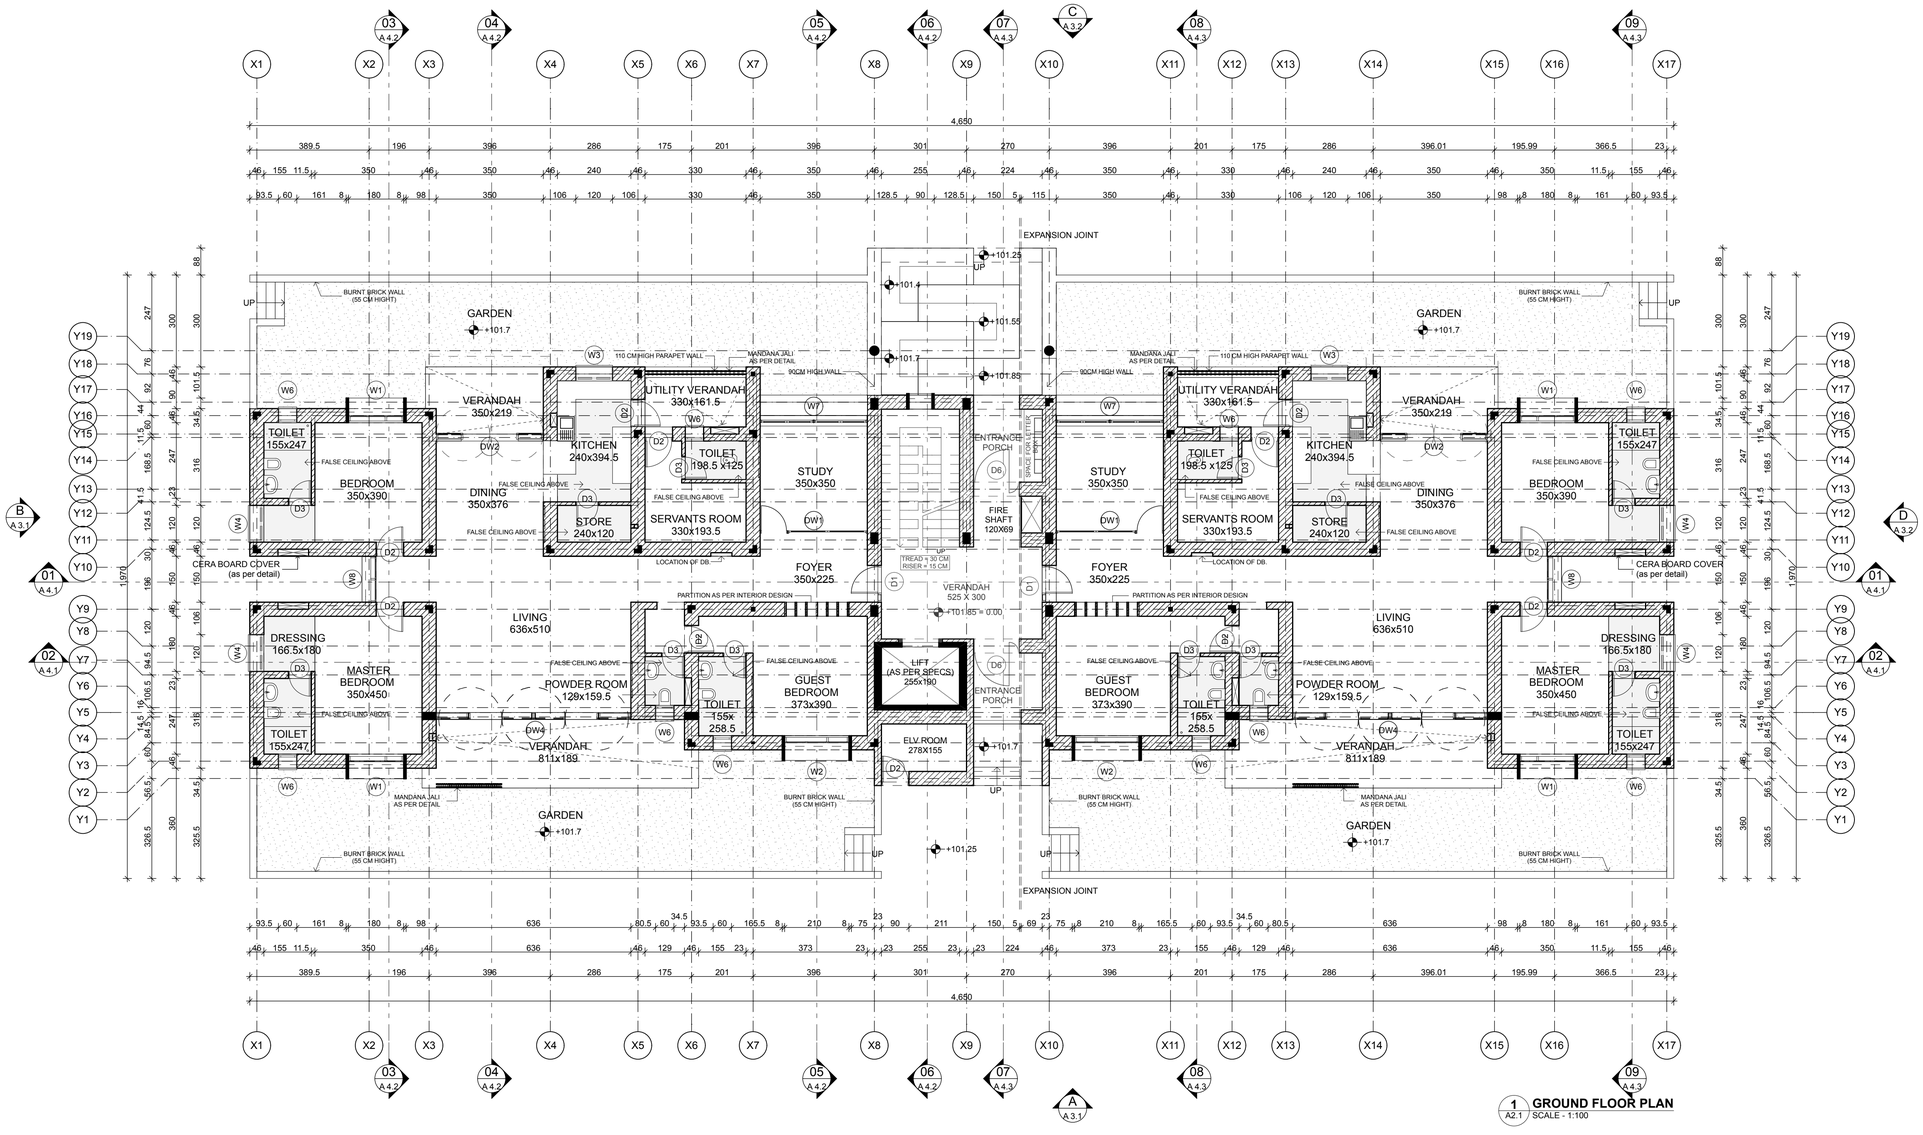

1 A2.1 **GROUND FLOOR PLAN**
SCALE - 1:100

NOTES

1. ALL DIMENSIONS SHALL BE CHECKED AND CO-RELATED WITH THE STRUCTURAL DRAWINGS AND ANY AMBIGUITY SHALL BE IMMEDIATELY BROUGHT TO THE NOTICE OF THE ARCHITECT BEFORE COMMENCEMENT OF THE WORK.
2. ALL DIMENSIONS ARE IN CENTIMETERS UNLESS AND OTHERWISE SPECIFIED
3. ALL LEVELS ARE FINISHED LEVELS.
4. ALL MARGINS, CLEARENCES ETC. REQUIRED AS PER BYE-LAWS SHOULD BE CHECKED AND PROVIDED BY THE CONTRACTOR AND ANY DESCRIPENCIES FOUND SHOULD BE IMMIDIATELY BROUGHT TO THE NOTICE OF ARCHITECT BEFORE COMMENCEMENT OF WORK.

DOOR SCHEDULE

NO.	WIDTH (cm)	HEIGHT (cm)	SILL (cm)	LINTEL (cm)	TYPE	APARTMENT TYPE
D1	120	225	-	225	SINGLE SHUTTER FLUSH DOOR WITH FLYMESH	1,2,3
D2	90	225	-	225	SINGLE SHUTTER FLUSH DOOR	1,2,3
D3	75	210	-	210	SINGLE SHUTTER FLUSH DOOR	1,2,3
D4	90	210	-	210	SINGLE SHUTTER FLUSH DOOR	1,2,3
D5	150	290	-	290	M.S GATE	1,2,3
-						
DW1	300	311.5	-	311.5	SINGLE SHUTTER FLUSH DOOR WITH DOUBLE SHUTTER WINDOW	1
DW2	350	290	-	290	DOUBLE SHUTTER FLYDOOR DOOR	1,2,3
DW3	165	225	-	225	SINGLE SHUTTER FLUSH DOOR WITH SINGLE SHUTTER WINDOW	3
DW4	636	290	-	290	DOUBLE SHUTTER FLYDOOR DOOR	1

WINDOW SCHEDULE

NO.	WIDTH (cm)	HEIGHT (cm)	SILL (cm)	LINTEL (cm)	TYPE	APARTMENT TYPE
W1	180	142.5	82.5	225	DOUBLE SHUTTER WOODEN WINDOW	1,2,3
W2	210	142.5	82.5	225	DOUBLE SHUTTER WOODEN WINDOW	1,2
W3	120	86.5	138.5	225	DOUBLE SHUTTER WOODEN WINDOW	1,2
W4	120	142.5	82.5	225	DOUBLE SHUTTER WOODEN WINDOW	1,2
W5	90	142.5	82.5	225	DOUBLE SHUTTER WOODEN WINDOW	3
W6	60	64.5	160.5	225	SINGLE SHUTTER WOODEN WINDOW	1,2,3
W7	300	373	17	290	DOUBLE SHUTTER WOODEN WINDOW	1
W8	150	208	17	225	DOUBLE SHUTTER WOODEN WINDOW	1
W9	120	208	17	225	DOUBLE SHUTTER WOODEN WINDOW	2
W10	120	108	182	290	FIX GLASS WINDOW	1,2,3

TENDER DRAWINGS

Key Plan

N

Consultants

- **Structural Consultants**
  VR SHAH Consulting Engineers
- **Services Consultants**
  DBHMS
- **Landscape Consultants**
  Earthscape Consultancy Pvt Ltd
- **Road and Pathways Consultants**
  Arhmm Infra Consultants LLP

Project

Nalanda University, Rajgir, Bihar

Title

Faculty Apartment

Type 1B- Ground Floor Plan

Dealt :	Janardhan	Drawing No. NUC(1)-FAH - A.2.1
Checked :	Piyas Choudhuri	
Scale :	As Shown	
Date :	13/02/17	

VĀSTU SHILPĀ CONSULTANTS
Architects I Planners I Urban Designers

'Sangath', Thaltej Road, Ahmedabad - 380054
Phone: 079 - 27454537 Fax: 079 - 27452006
www.sangath.org e-mail: **vsc@sangath.org**