PODIUM AREA DIAGRAM
SCALE - 1:1000

AS PER CTS NO. 1,
CTS NO. 3

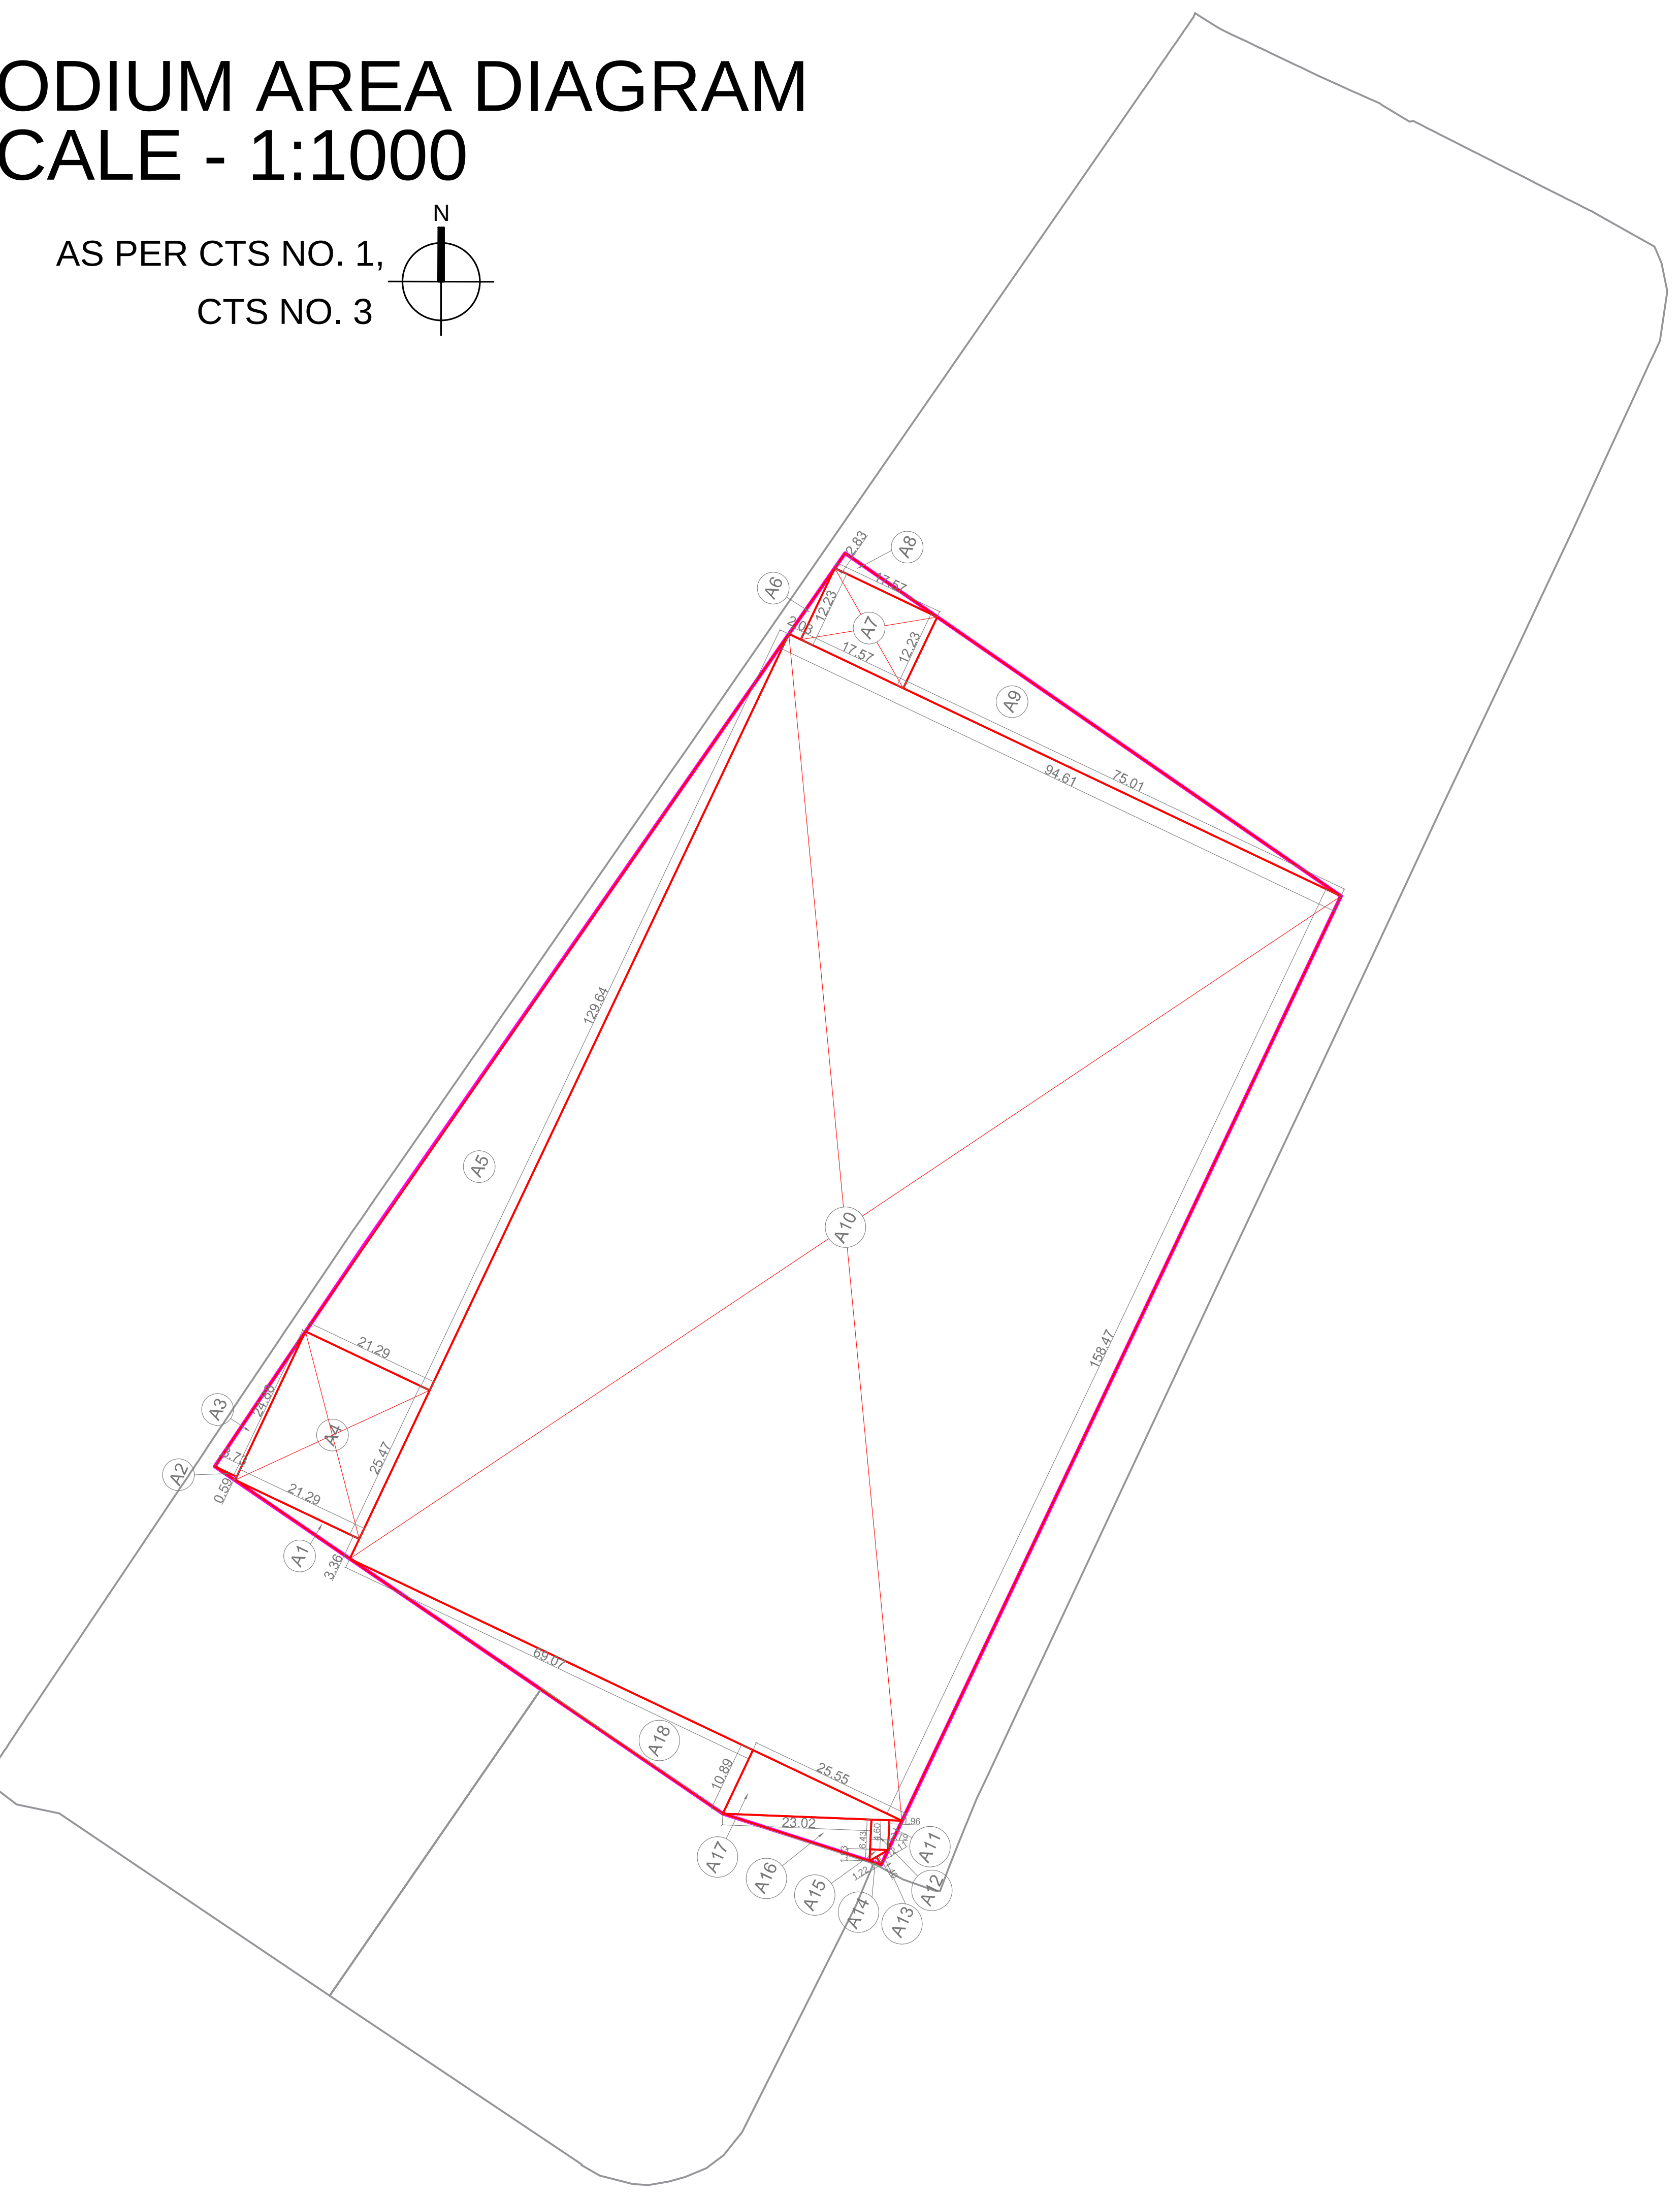

PODIUM LEVEL CALCULATION				
DESCRIPTION	DIMENSION (IN METERS)			AREA (IN
	FACTOR	BASE	HEIGHT	
A1	0.5	3.36	21.29	35.767
A2	0.5	0.59	3.73	1.1004
A3	0.5	3.73	24.88	46.401
A4	1	21.29	25.47	542.26
A5	0.5	21.29	129.64	1380
A6	0.5	2.03	12.23	12.413
A7	1	17.57	12.23	214.88
A8	0.5	2.83	17.57	24.862
A9	0.5	12.23	75.01	458.69
A10	1	158.47	94.61	14993
A11	0.5	1.96	4.6	4.508
A12	1	2.79	4.6	12.834
A13	0.5	1.4	2.11	1.477
A14	0.5	1.22	1.4	0.854
A15	0.5	1.83	2.79	2.5529
A16	0.5	6.43	23.02	74.009
A17	0.5	10.89	25.55	139.12
A18	0.5	10.89	69.07	376.09
TOTAL AREA				18321

TOTAL AREA PER PODIUM LEVEL	18320.7 SQ.M
TOTAL AREA OF 3 PODIUM LEVELS	54962.1 SQ.M

PARKING REQUIREMENT		
BUILDINGS	TWO WHEELER	FOUR WHEELER
BUILDING 2	132	66
BUILDING 3	220	110
BUILDING 4	220	110
BUILDING 5	143	72
BUILDING 6	176	88
BUILDING 7	143	72
TOTAL PARKING	1034	518

PODIUM PARKING PROPOSED		
PODIUM	TWO WHEELER	FOUR WHEELER
P1	382	132
P2	387	234
P3	387	234
TOTAL PARKING	1156	600

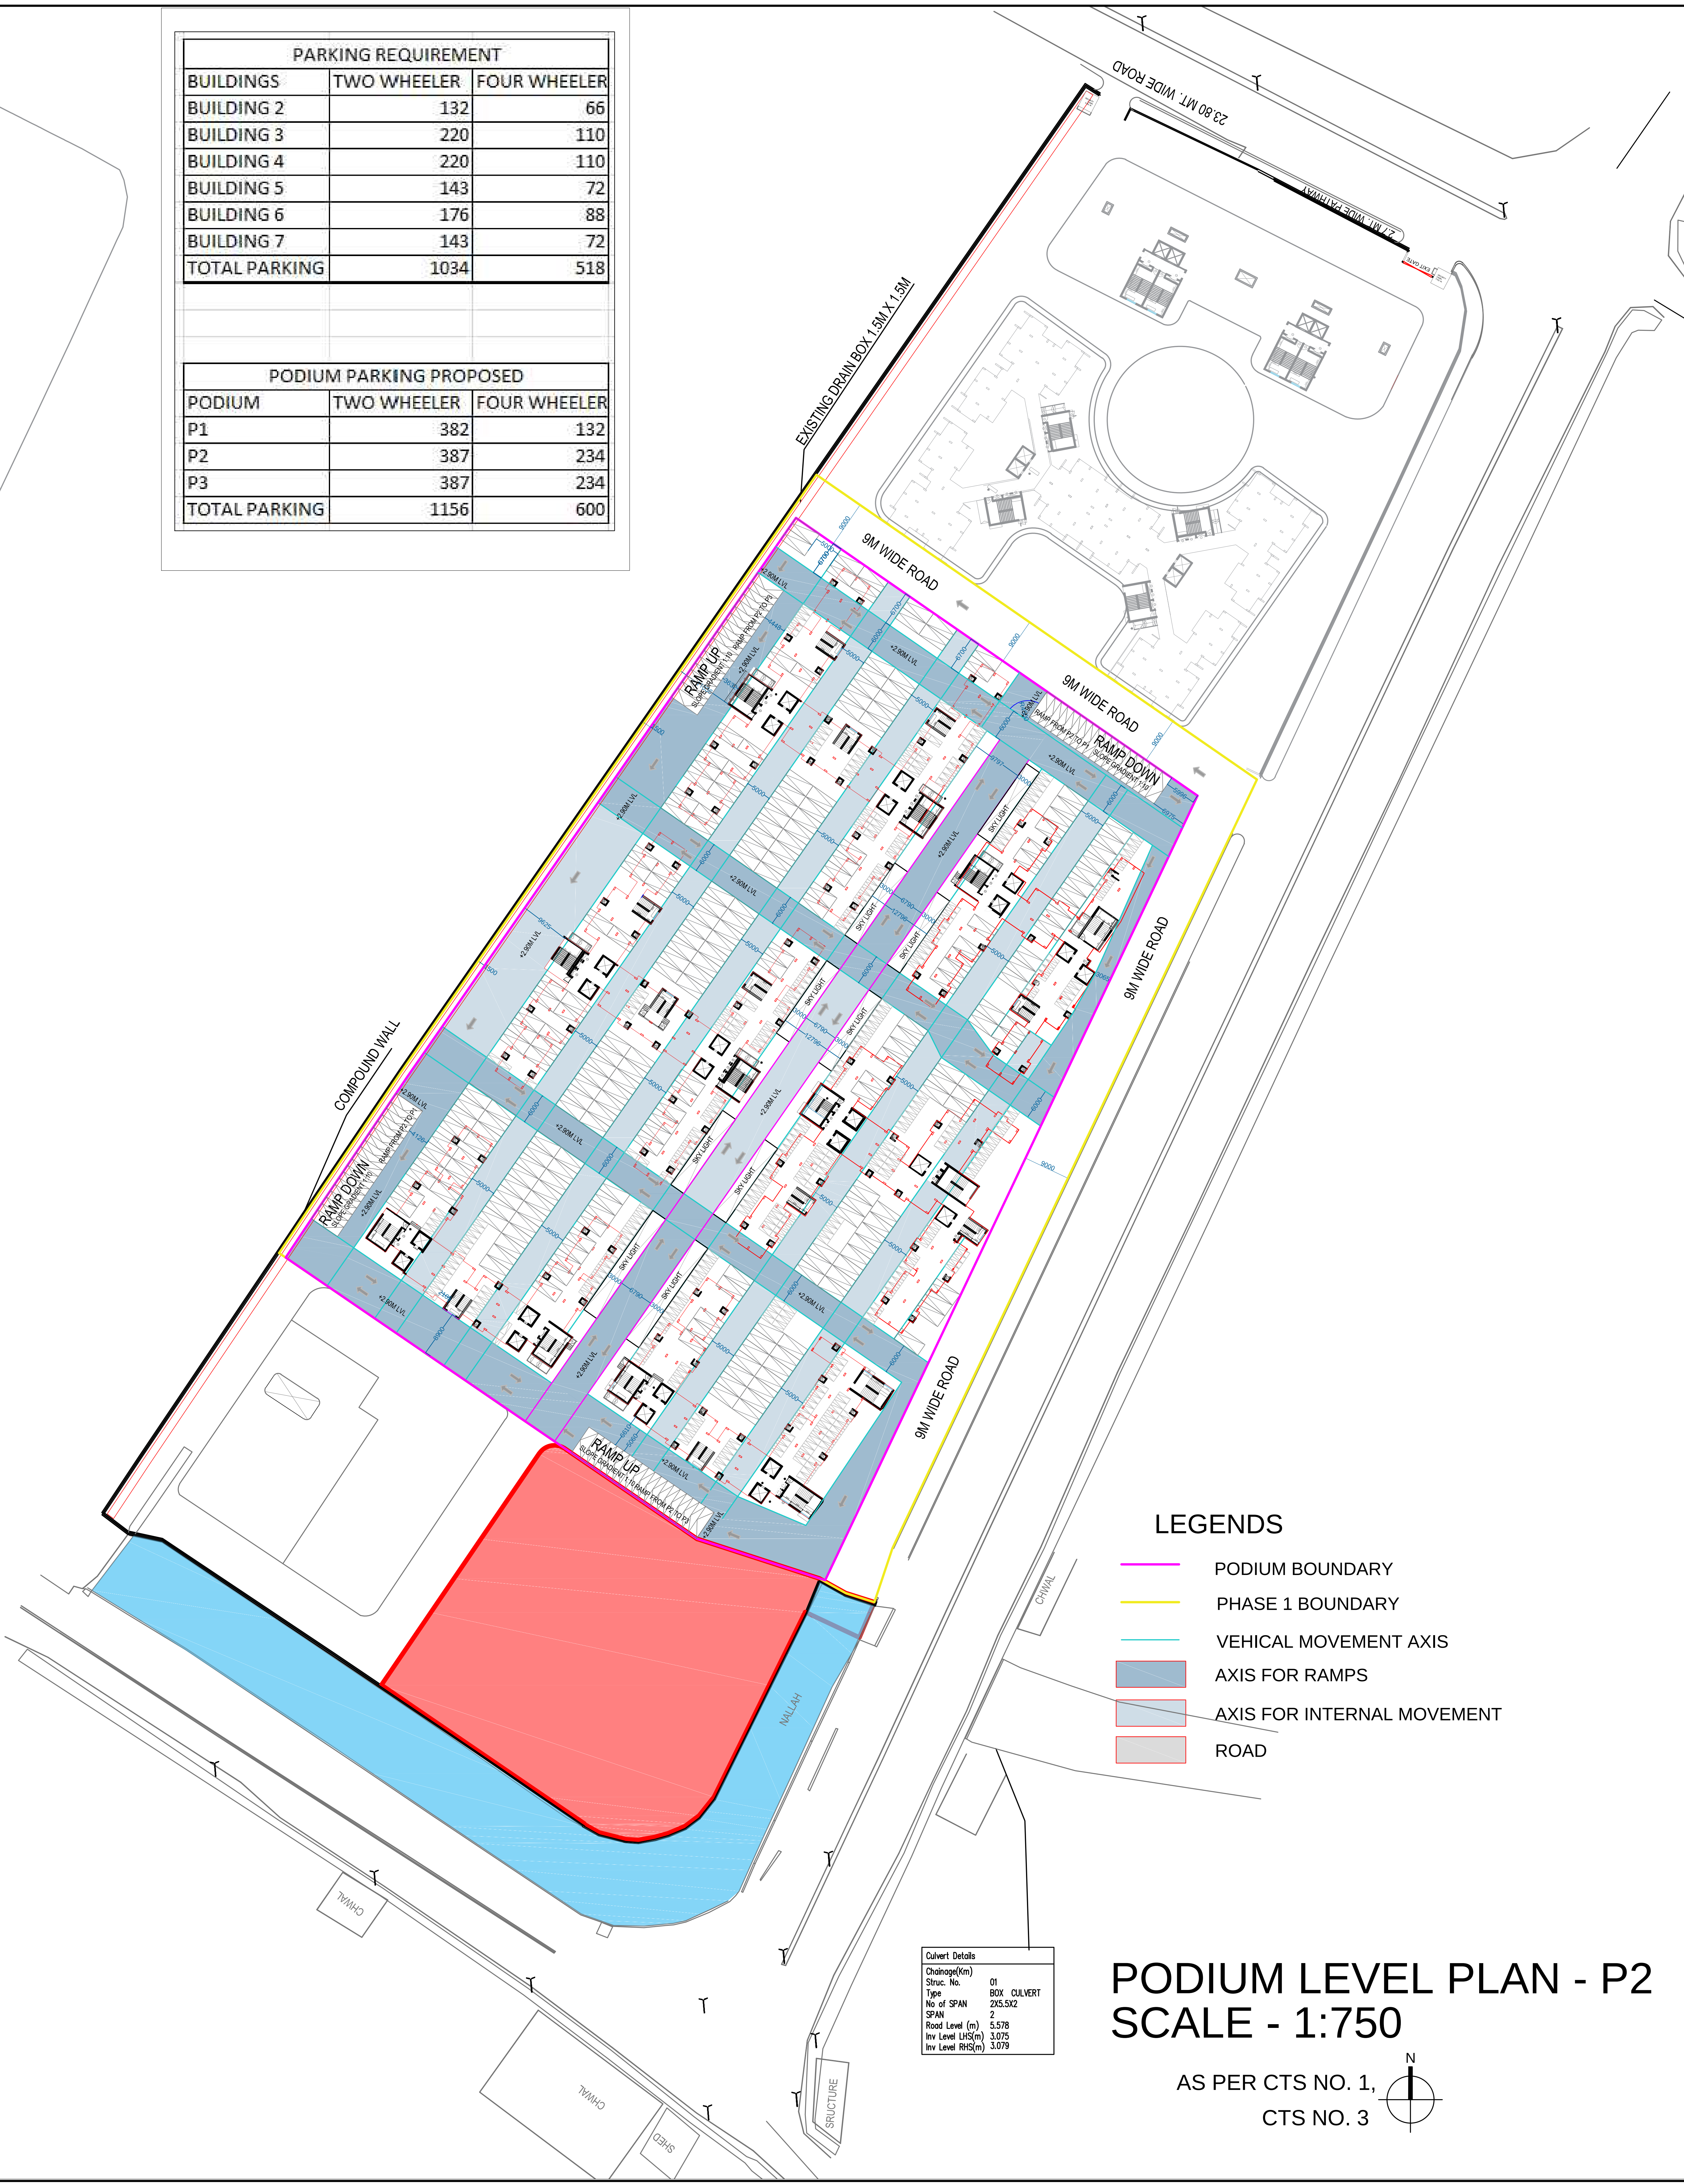

Culvert Details
Chainage(Km)
Struc. No. 01
Type BOX CULVERT
No of SPAN 2X5.5X2
SPAN 2
Road Level (m) 5.578
Inv Level LHS(m) 3.075
Inv Level RHS(m) 3.079

LEGENDS

—	PODIUM BOUNDARY
—	PHASE 1 BOUNDARY
—	VEHICAL MOVEMENT AXIS
▨	AXIS FOR RAMPS
▨	AXIS FOR INTERNAL MOVEMENT
▨	ROAD

PODIUM LEVEL PLAN - P2
SCALE - 1:750

AS PER CTS NO. 1,
CTS NO. 3

SHEET NO :

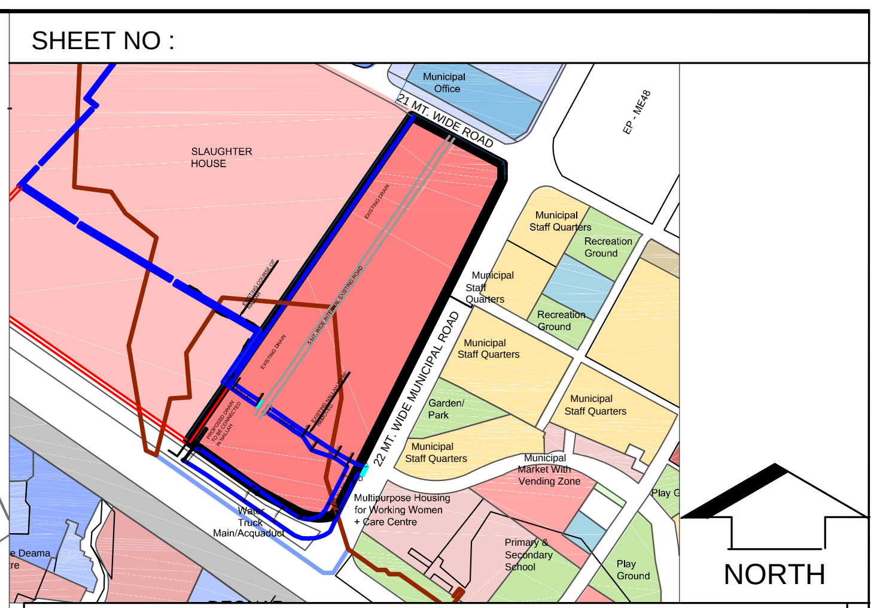

LOCATION PLAN SCALE 1:4000

CONTENT OF SHEET :

LOCATION PLAN, GIS PLAN, DP PLAN
BLOCK PLAN
STILT FLOOR PLAN
AREA, WATER AND PARKING CALCULATIONS

SITE	▬
NALLAH	—

COLOURING OF PLANS AS PER DCPR-34

—	THICK BLACK PLOT BOUNDARY	—	RED DOTTED DRAINAGE & SEWERAGE WORK
—	GREEN EXISTING STREET	—	BLUE DOTTED THIN WATER SUPPLY
—	GREEN DOTTED FUTURE STREET	▨	RED HATCHED DEVIATIONS
—	THICK BLACK DOTTED PERM. BLDG	🟩	GREEN WASH RECREATION GROUND
	NO COLOUR OPEN SPACES	—	BURNT SIENNA ROADS & SETBACKS
▨	YELLOW HATCHED DEMOLISHED WORK		APPROPRIATE COLOUR CODE RESERVATIONS
🟥	RED FILLED PROPOSED WORK		

CERTIFICATE

"THIS IS TO CERTIFY THAT THE SCOPE OF WORK HAS BEEN EXPLAINED TO ME BY THE ARCHITECT / CONSULTANT AND CONSIDERING THE BUDGET PROVISION THEREFORE I AM SATISFIED WITH THE PROJECT PROPOSAL"

NOTE : USER SIGNATURE IS PROVIDED IN THE SCANNED COPY OF THE PLANS AND HENCE IT IS REQUESTED THAT THE SAME IS NOT INSISTED ON DIGITAL PRINTS, IN CASE REQUIRED , THE SAME WILL BE OBTAINED BEFORE STARTING OF THE WORK.

ARCHITECT MASTER & ASSOCIATES

MUNICIPAL ARCHITECT

R1	08-08-2022	AREA STATEMENT REVISED	URVASHI
R0	03-08-2022	PODIUM PARKING LAYOUT	URVASHI

FILE PATH :
PC NO. 11 \D:\Drawings\MILONI\1896-- 600 TENEMENTS, DEONAR

TYPE OF DWG :
APPROVAL DRAWING

CLIENT:
MUNICIPAL CORPORATION OF GREATER MUMBAI (MCGM)

TITLE OF DRAWING :PODIUM LEVEL PLAN - P2

PROPOSED REDEVELOPMENT ON OPEN PLOT,
KNOWN AS '600 TENEMENTS PLOT BEARING CTS NO. 1(PT) &
CTS NO. 3(PT) OF VILLAGE DEONAR IN M/EAST WARD IN MUMBAI
JOB TITLE :

DRAWN BY : URVASHI	N	PROJECT CODE: 1896
CHECKED BY :UDM		DRAWING NO: 1896-509
SCALE: AS MENTIONED	DATE : 1.08.2022	REVISION NO: R1

THIS DRAWING IS THE PROPERTY OF
MASTER & ASSOCIATES
ARCHITECTS, INTERIOR DESIGNERS & PROJECT MANAGEMENT CONSULTANTS
AND IS NOT TO BE REPRODUCED, COPIED HANDED OVER TO A THIRD PARTY OR USED FOR ANY PURPOSE OTHER THAN FOR WHICH IT HAS BEEN LOANED

STATUS

MASTER & ASSOCIATES
ARCHITECTS, INTERIOR DESIGNERS &
PROJECT MANAGEMENT CONSULTANTS

MUMBAI
HAMAM HOUSE,34-38 AMBALAL DOSHI MARG,
MUMBAI - 400 001, India.
PHONE NO +91-22-2265 4606 / 4736 FAX 22700173
EMAIL ADD : • udaymaster@rediffmail.com
• udaymaster@gmail.com

ALGIERS
SLIMANE ABD ELAZIZ, CITE 18 LOGEMENTS BLOC - B1, N °3,
CILLE DE REHMANIA, ZERALDA ALGIERS.
PHONE NO 00213-071076049
EMAIL ADD : • udaymasteralgeria@gmail.com
MOBILE : 213-93397968

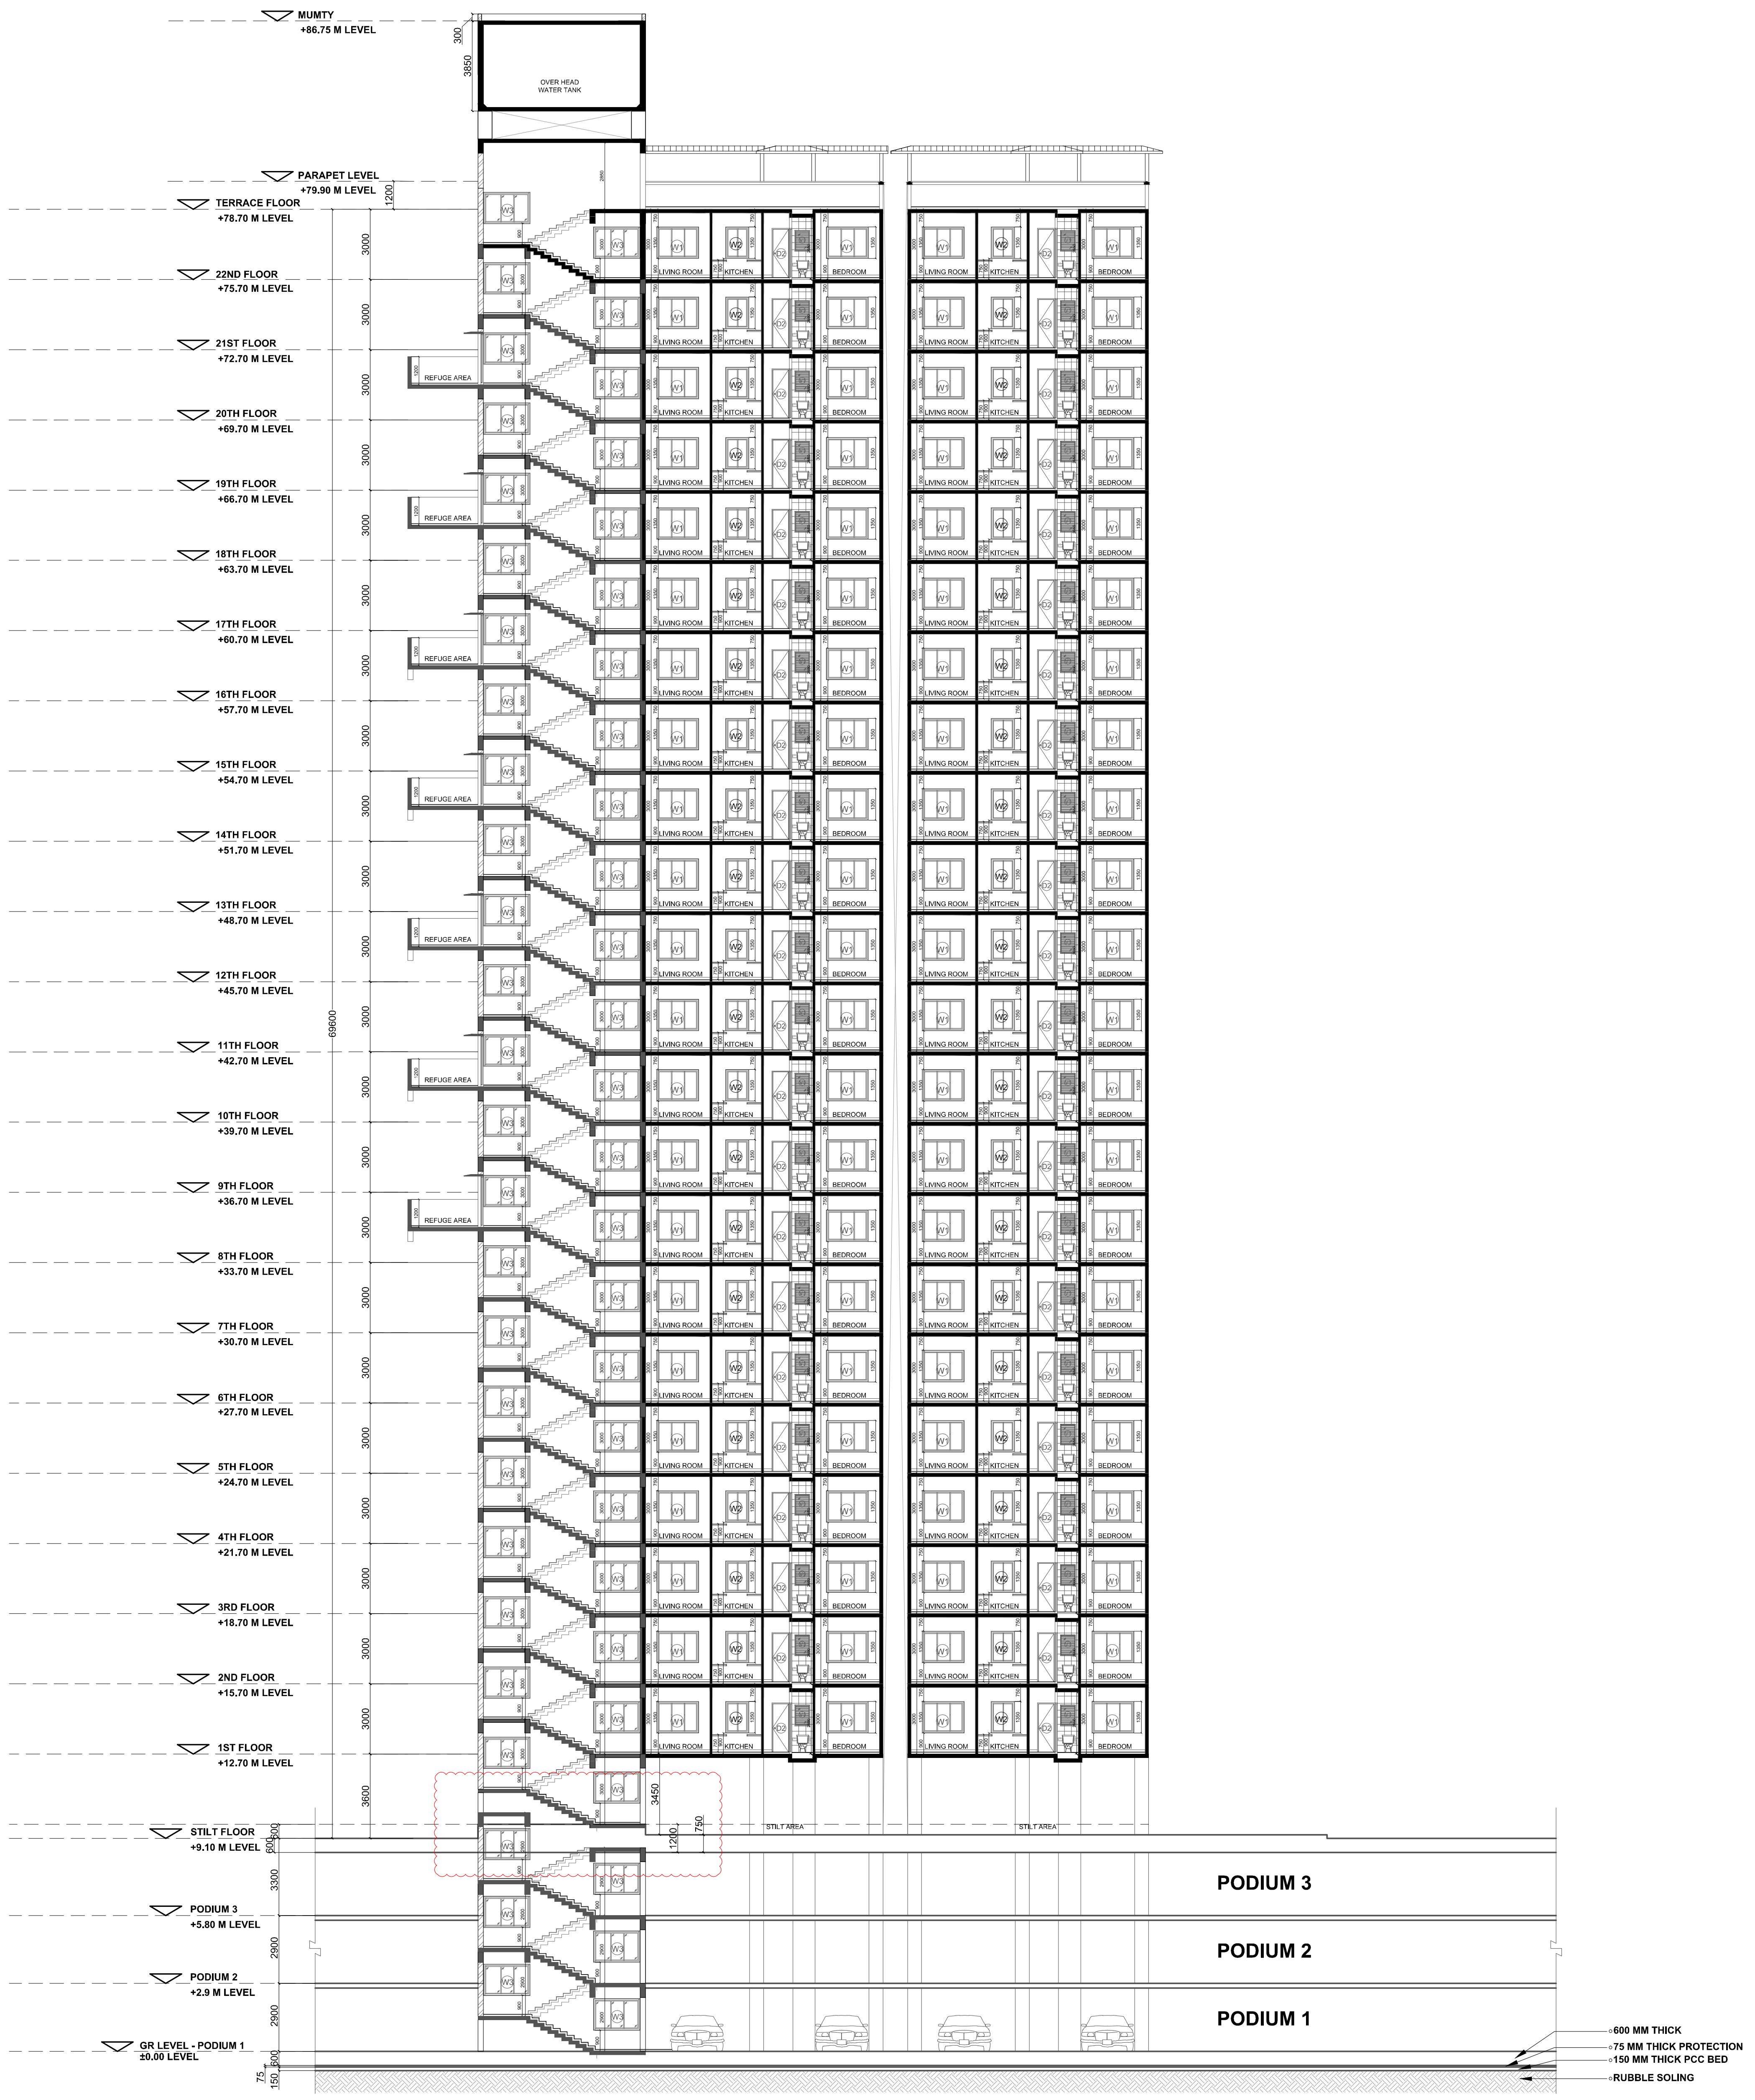

SECTION - BB'

SECTION B-B'
SCALE 1:100

PRINTS ISSUED TO											
PRINTS ISSUED FOR											
NO. OF PRINTS											
DATE											
BY											

COLOURING OF PLANS AS PER DCPR-34

—	THICK BLACK PLOT BOUNDARY	—	RED DOTTED DRAINAGE & SEWERAGE WORK
—	GREEN EXISTING STREET	—	BLUE DOTTED THIN WATER SUPPLY
—	GREEN DOTTED FUTURE STREET	▨	RED HATCHED DEVIATIONS
—	THICK BLACK DOTTED PERM. BLDG	🟩	GREEN WASH RECREATION GROUND
	NO COLOUR OPEN SPACES	—	BURNT SIENNA ROADS & SETBACKS
▨	YELLOW HATCHED DEMOLISHED WORK		APPROPRIATE COLOUR CODE RESERVATIONS
🟥	RED FILLED PROPOSED WORK		

THIS DRAWING IS THE PROPERTY OF
MASTER & ASSOCIATES ARCHITECTS, INTERIOR DESIGNERS & PROJECT MANAGEMENT CONSULTANTS
AND IS NOT TO BE REPRODUCED, COPIED, HANDED OVER TO A THIRD PARTY OR USED FOR ANY PURPOSE OTHER THAN THAT FOR WHICH IT HAS BEEN LOANED

STATUS

BUILDING 02 - SHEET NO : 04 OF 06

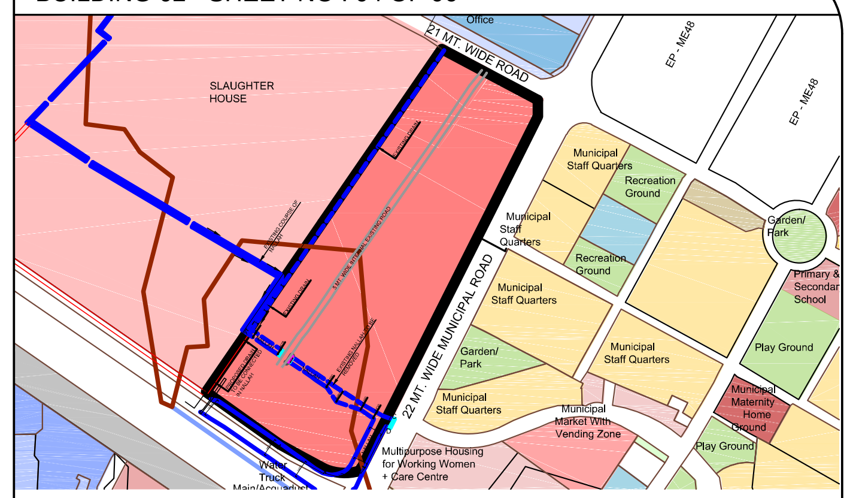

LOCATION PLAN SCALE 1:4000

CONTENT OF SHEET :
SECTION B-B'
SECTION C-C'

KEY PLAN SCALE 1:500

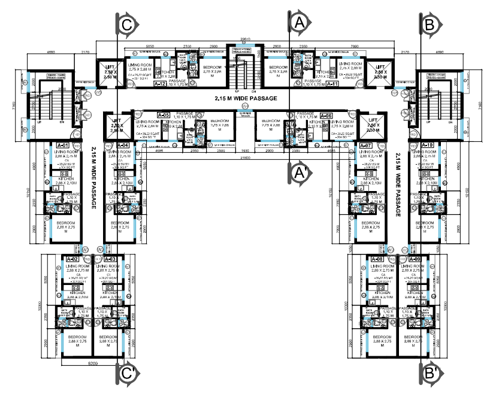

AD-FO	D-FO	DY-CFO
SE-BP	AE-BP	EE-BP

CERTIFICATE

"THIS IS TO CERTIFY THAT THE SCOPE OF WORK HAS BEEN EXPLAINED TO ME BY THE ARCHITECT / CONSULTANT AND CONSIDERING THE BUDGET PROVISION THEREFORE I AM SATISFIED WITH THE PROJECT PROPOSAL"

NOTE : USER SIGNATURE IS PROVIDED IN THE SCANNED COPY OF THE PLANS AND HENCE IT IS REQUESTED THAT THE SAME IS NOT INSISTED ON DIGITAL PRINTS, IN CASE REQUIRED , THE SAME WILL BE OBTAINED BEFORE STARTING OF THE WORK.

AC-Estate

ARCHITECT MASTER & ASSOCIATES
MUNICIPAL ARCHITECT

REVISION	DATE	DESCRIPTION	BY
R0	12-08-2022	BUILDING 02 - SECTION B-B' & SECTION C-C'	URVASHI

FILE PATH :
PC NO. 11 \D:\Drawings\MILONI\1896-- 600 STAFF QUARTERS, DEONAR

TYPE OF DWG :
APPROVAL DRAWING

CLIENT:
MUNICIPAL CORPORATION OF GREATER MUMBAI (MCGM)

TITLE OF DRAWING :
TYPICALSECTION B-B'

PROPOSED REDEVELOPMENT ON OPEN PLOT,
KNOWN AS '600 TENEMENTS PLOT BEARING CTS NO. 1(PT) &
CTS NO. 3(PT) OF VILLAGE DEONAR IN M/EAST WARD IN MUMBAI
JOB TITLE :

DRAWN BY : URVASHI
CHECKED BY :
SCALE: AS MENTIONED
N
DATE :24-02-2022
PROJECT CODE: 1896
DRAWING NO: 1896-512
REVISION NO: R0

THIS DRAWING IS THE PROPERTY OF
MASTER & ASSOCIATES
ARCHITECTS, INTERIOR DESIGNERS &
PROJECT MANAGEMENT CONSULTANTS
AND IS NOT TO BE REPRODUCED, COPIED HANDED OVER TO A THIRD PARTY OR USED FOR ANY PURPOSE OTHER THAN FOR WHICH IT HAS BEEN LOANED

STATUS

MASTER & ASSOCIATES
ARCHITECTS, INTERIOR DESIGNERS &
PROJECT MANAGEMENT CONSULTANTS

MUMBAI
HAMAM HOUSE,34-38 AMBALAL DOSHI MARG,
MUMBAI - 400 001, India.
PHONE NO +91-22-2265 4606 / 4736 FAX 22700173
EMAIL ADD : • udaymaster@rediffmail.com
• udaymaster@gmail.com

ALGIERS
SLIMANE ABD ELAZIZ, CITE 18 LOGEMENTS BLOC - B1, N °3,
CILLE DE REHMANIA, ZERALDA ALGIERS.
PHONE NO 00213-071076049
EMAIL ADD : • udaymasteralgeria@gmail.com
MOBILE : 213-93397968